


c:\pwworking\east01\1626747\MBTA-HPA-TMP-046_048.dwg

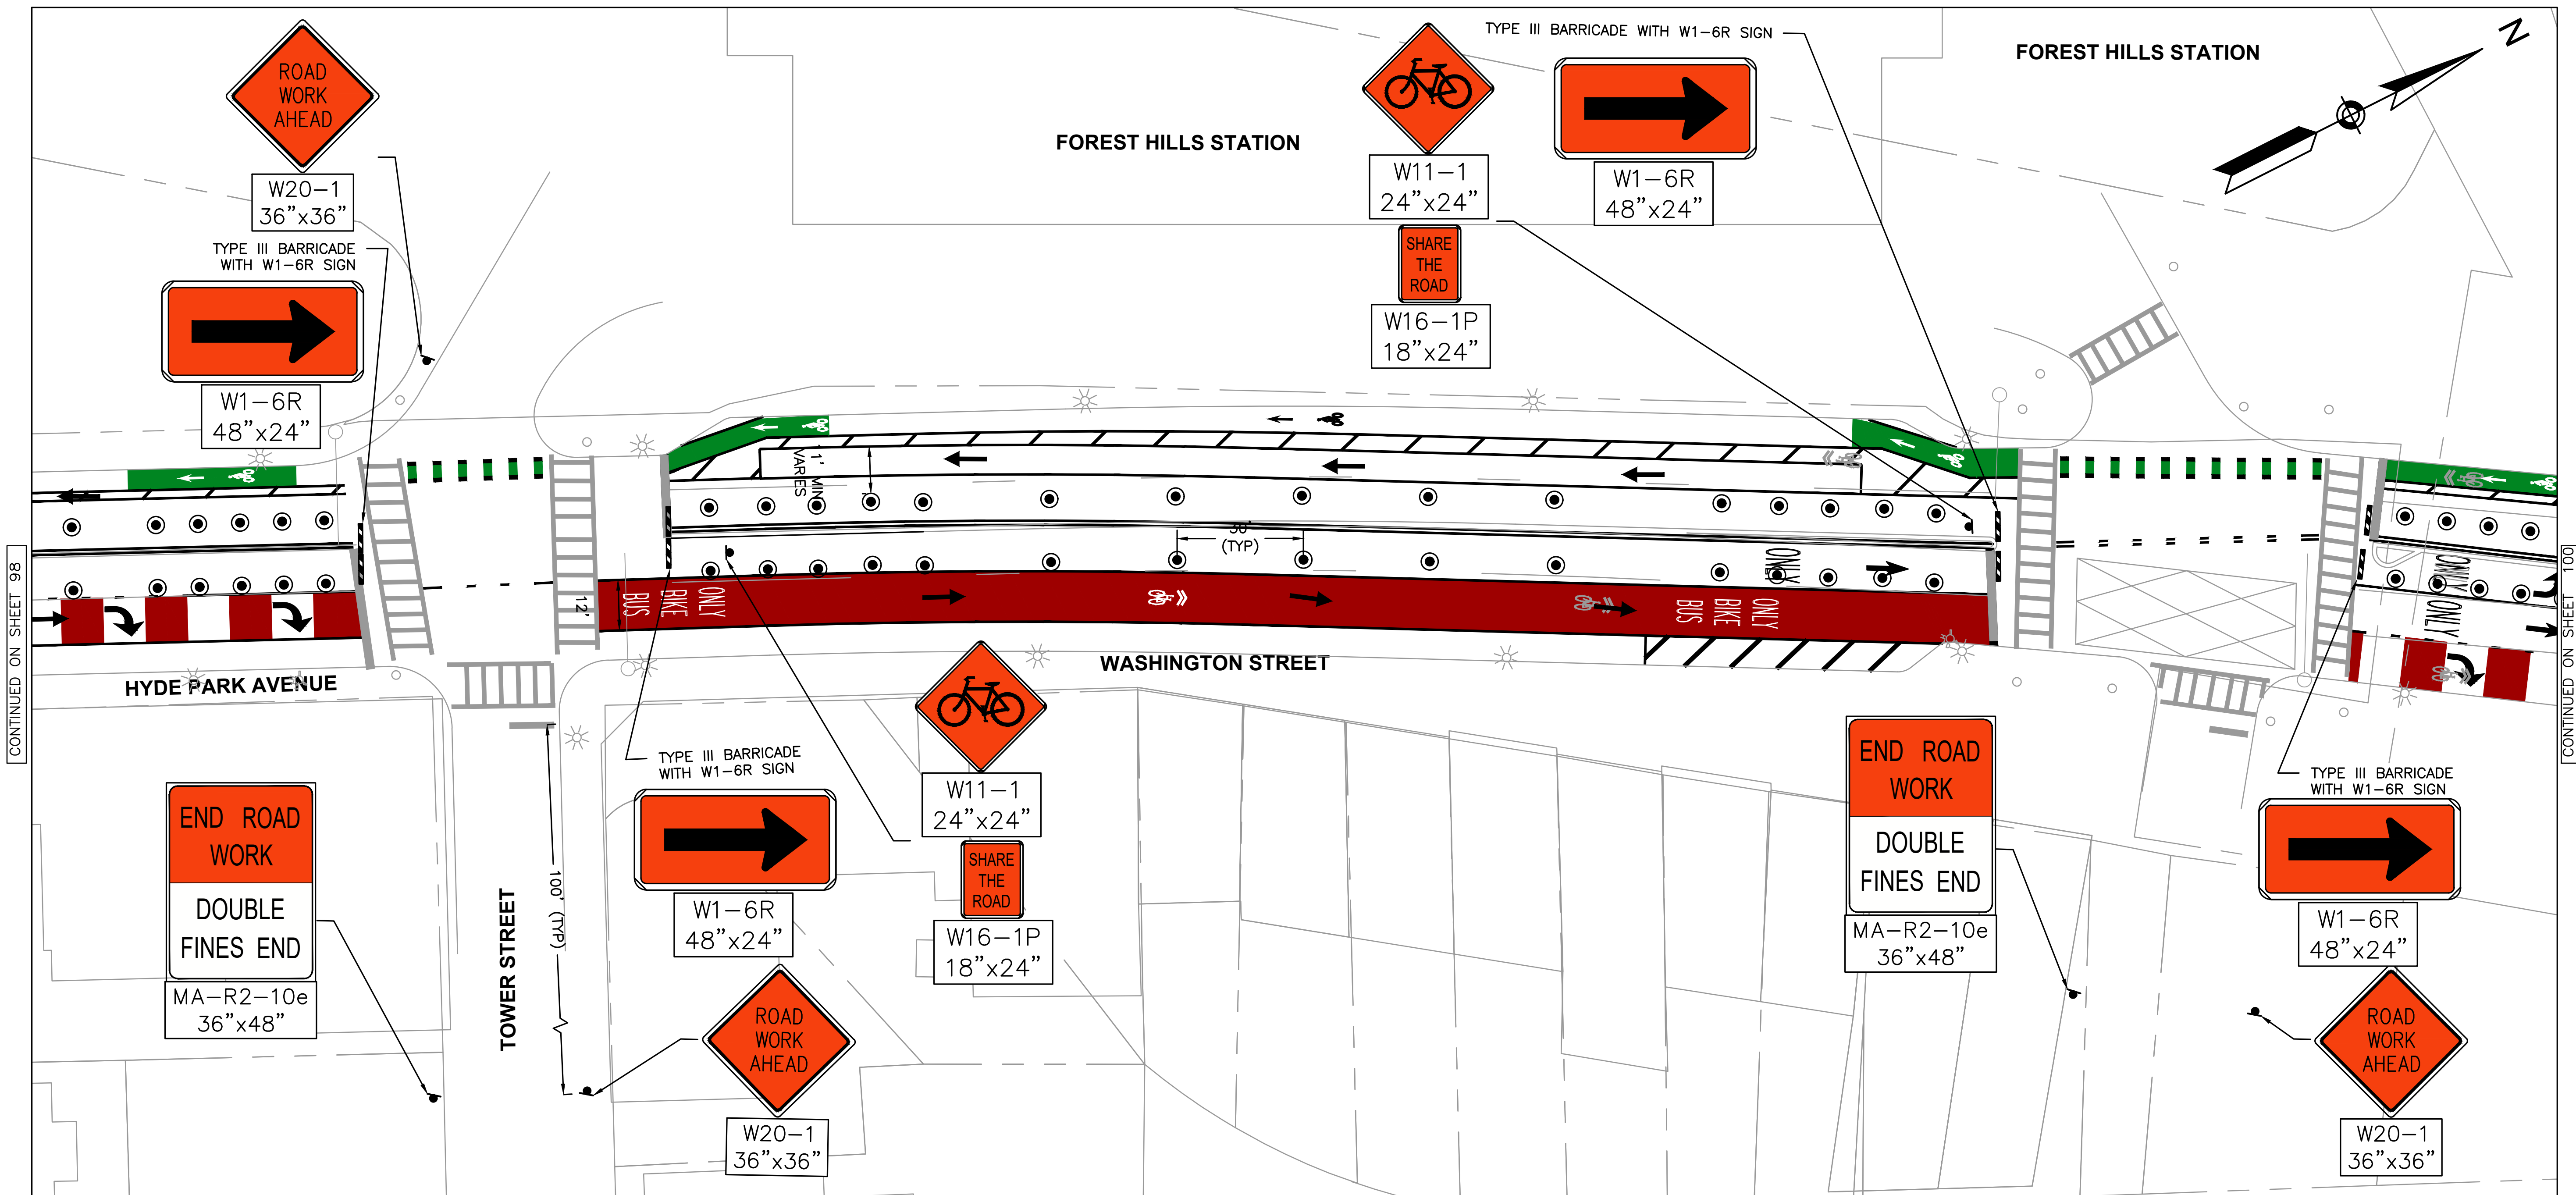

NOTES

1. EXISTING ACCESS TO DRIVEWAYS AND PUBLIC/RESIDENTIAL ENTRANCES TO BE MAINTAINED AT ALL TIMES THROUGHOUT CONSTRUCTION.

DRAFT
NOT FOR CONSTRUCTION

20 0 20 40
SCALE IN FEET

HDR HDR ENGINEERING, INC.
99 HIGH STREET, SUITE 2300
BOSTON, MASSACHUSETTS 02110-2378
(617) 357-7700

BTD
BOSTON
TRANSPORTATION
DEPARTMENT

DESIGNED BY	JCGC
DRAWN BY	JCGC
CHECKED BY	ML
APPROVED BY	RCP

30% DESIGN PROGRESS PRINT

CITY OF BOSTON TRANSPORTATION DEPARTMENT
ENGINEERING DIVISION
MBTA CONTRACT Z91PS33
BUS SYSTEM INFRASTRUCTURE IMPROVEMENTS
HYDE PARK AVENUE
NB_SB OUTSIDE LANE TRAFFIC
MANAGEMENT PLAN

AREA: -	BOSTON	AUGUST 2020
DISTRICT: #		DRAWING NO. TMP-047
		SHEET 99 OF 101

DRAWING PREPARED BY HDR ENGINEERING, INC.