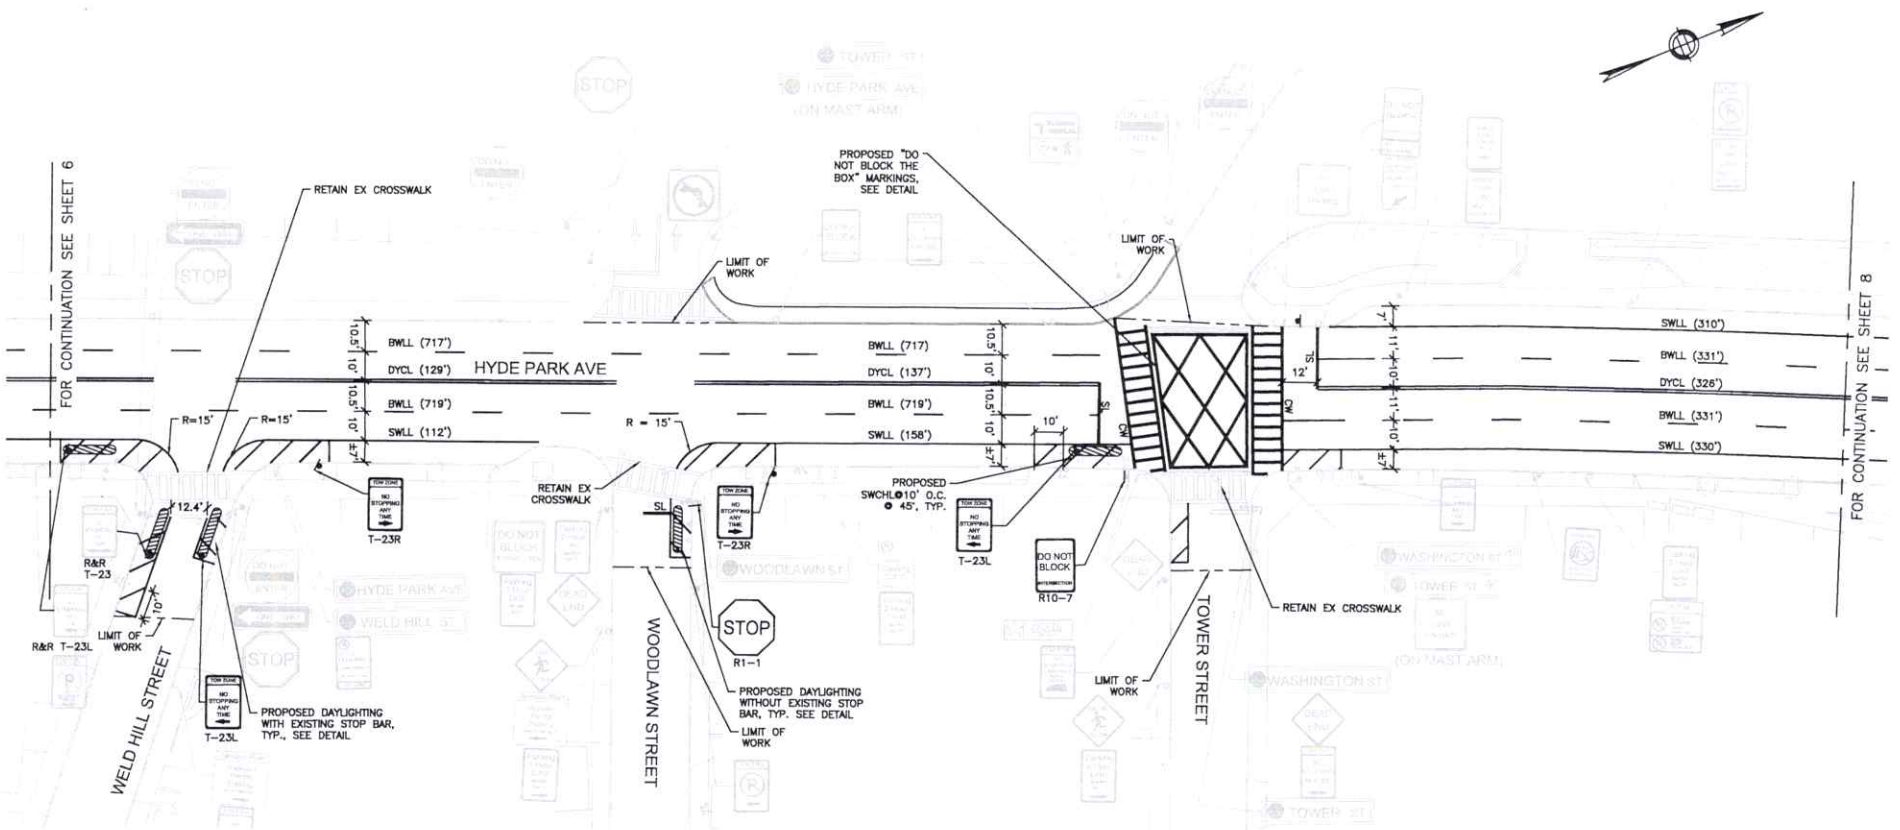



NOT FOR CONSTRUCTION

NOTE:
1. NEW SIGNS SHALL BE FULLY INSTALLED AT THE SAME TIME OR PRIOR TO THE INSTALLATION OF NEW PAVEMENT MARKINGS.
2. SIGNS CONFLICTING WITH EXISTING PAVEMENT MARKINGS SHALL BE COVERED UNTIL THE FINAL PAVEMENT MARKINGS ARE INSTALLED. ONCE THE NEW PAVEMENT MARKINGS ARE INSTALLED, SIGNS SHALL BE PROMPTLY UNCOVERED.
3. NEW TRAFFIC CONTROL DEVICES AND SIGNS (INCLUDING CURB-USE SIGNS) SHALL NOT BE INSTALLED, MODIFIED, OR RELOCATED IN A WAY THAT IMPEDES THE CONTINUOUS, ACCESSIBLE, UNOBSTRUCTED PATH FOR PEDESTRIANS.
4. THE MINIMUM HEIGHT, MEASURED VERTICALLY FROM THE BOTTOM OF THE SIGN TO SIDEWALK, SHALL BE 7 FEET.
5. ALL SIGNS TO BE RETAINED UNLESS OTHERWISE NOTED.

TOOLE DESIGN
141 TREMONT ST
9TH FLOOR
BOSTON, MA 02111

City of Boston Transportation

| | |
|---|---|
| DESIGNED BY: | J. TILLISON |
| DRAWN BY: | J. TILLISON |
| CHECKED BY: | S. ADHIKARI |
| APPROVED BY: | P. BUEHRER |

CITY OF BOSTON TRANSPORTATION DEPARTMENT
ENGINEERING DIVISION
CORRIDOR IMPROVEMENT PLANS

# HYDE PARK AVE
## PAVEMENT MARKING AND SIGNAGE PLANS

| | | | |
|---|---|---|---|
| DISTRICT: | 6 | DATE: | 7/24/2026 |
| SCALE: | 1":20' | SHEET: | 7 OF 12 |